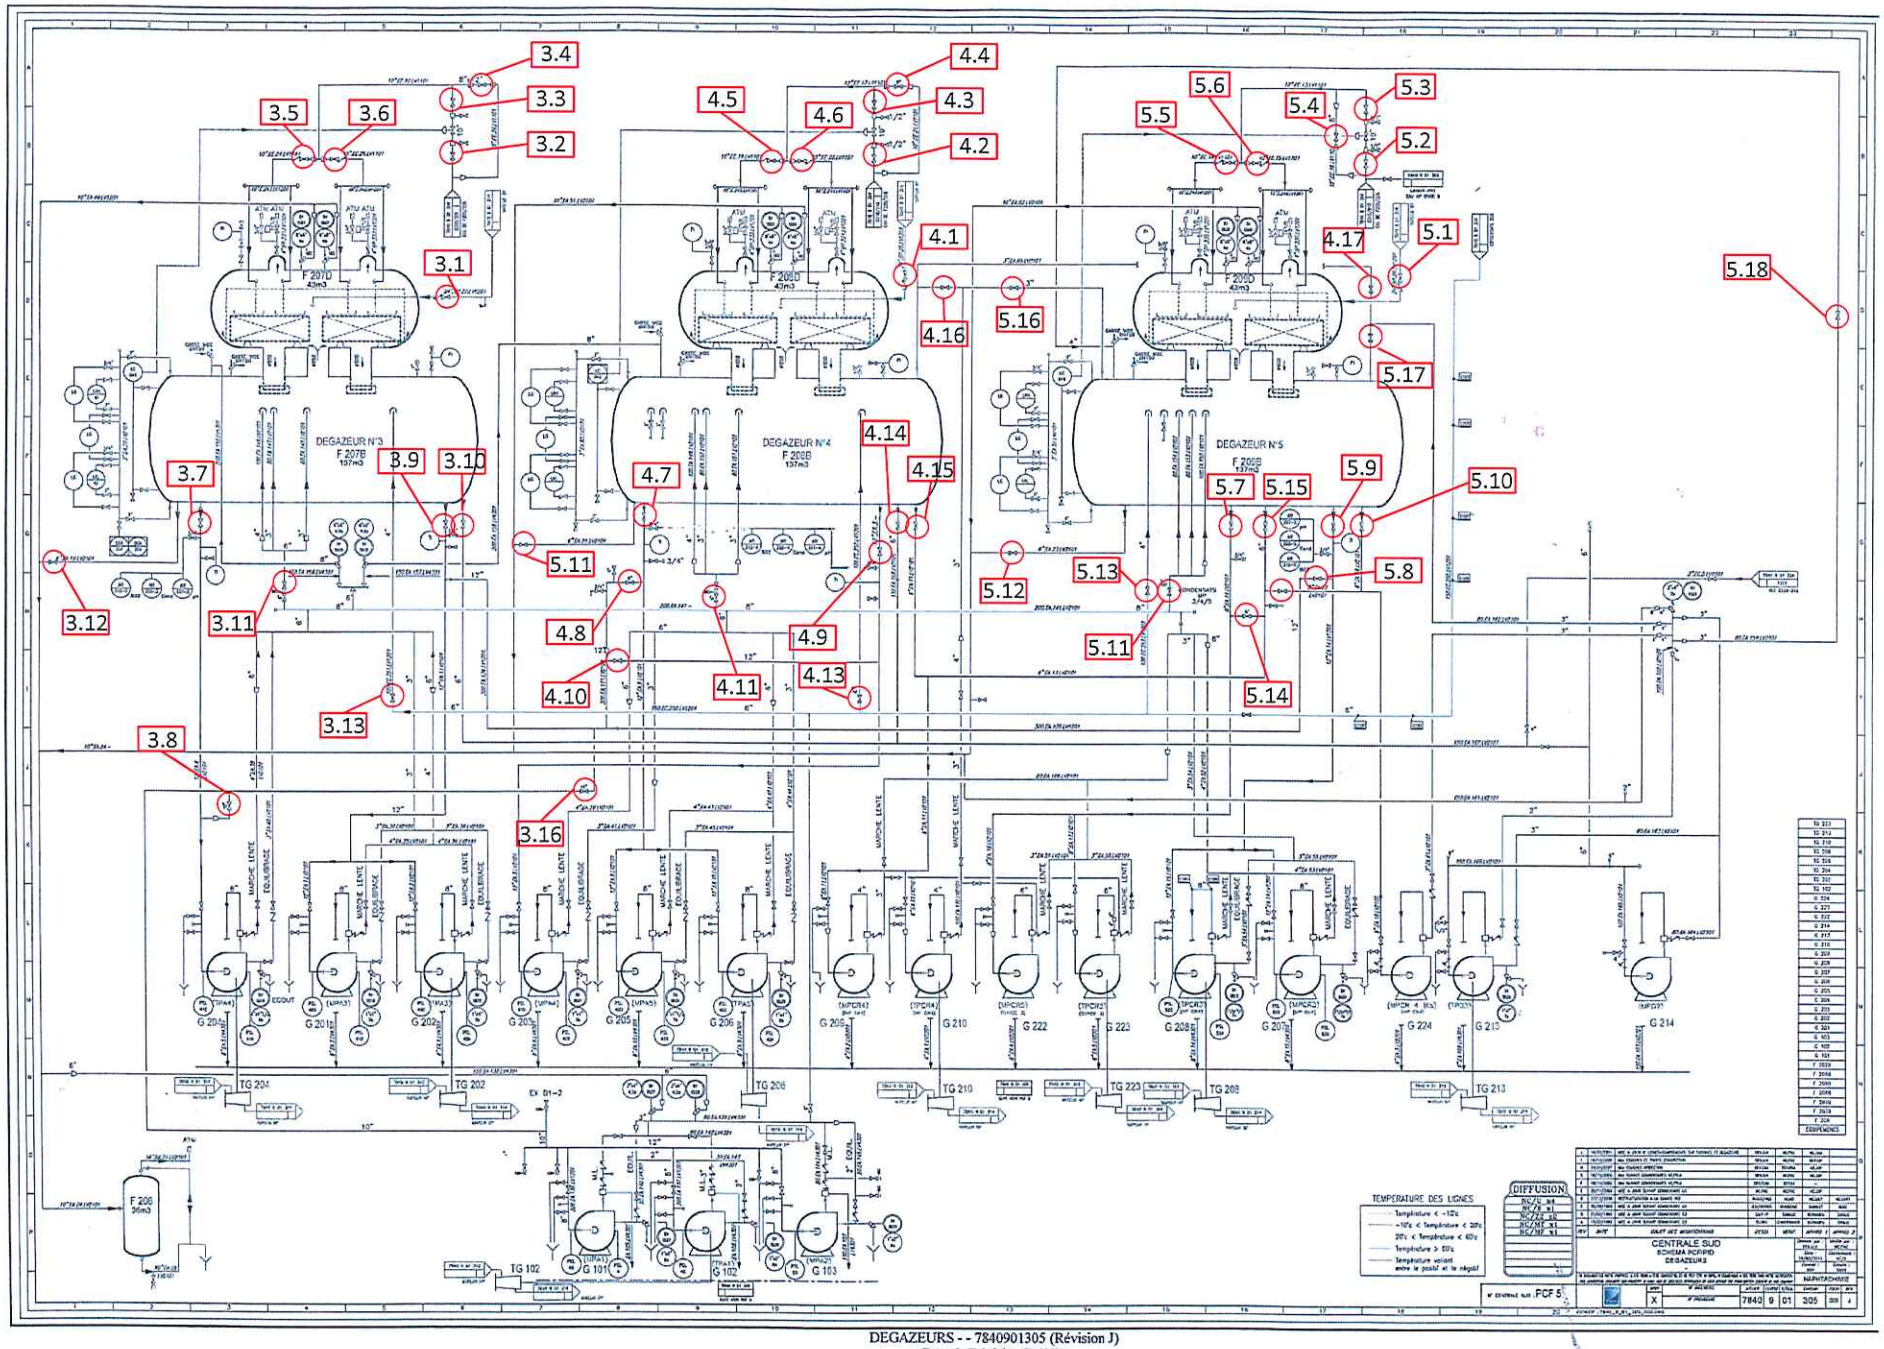

3.4
3.3
3.2
3.5
3.6
3.1
4.4
4.3
4.2
4.5
4.6
4.1
4.16
5.16
5.6
5.3
5.4
5.2
5.5
4.17
5.1
5.18
5.17
F 207D
43m3
F 208D
43m3
F 209D
43m3
DEGAZEUR N°3
F 207B
137m3
DEGAZEUR N°4
F 208B
137m3
DEGAZEUR N°5
F 209B
137m3
3.7
3.9
3.10
4.7
4.14
4.15
5.7
5.15
5.9
5.10
5.11
5.12
5.13
5.8
3.12
3.11
4.8
4.9
4.10
4.11
4.13
5.11
5.14
3.13
3.8
3.16
MARCHE LENTE
EQUILIBRAGE
G 201
G 201S
G 202
G 203
G 204
G 205
G 206
G 209
G 210
G 222
G 223
G 208
G 207
G 224
G 213
G 214
TG 204
TG 202
TG 206
TG 210
TG 223
TG 208
TG 213
EX D1-2
F 206
36m3
TG 102
G 101
G 102
G 103
TEMPERATURE DES LIGNES
Température < -10°c
-10°c < Température < 20°c
20°c < Température < 60°c
Température > 60°c
Température variant
entre le positif et le négatif
DIFFUSION
RC/E_N1
RC/E_N2
RC/ME_N1
RC/INF_N1
CENTRALE SUD
SCHEMA PCRIPD
DEGAZEURS
NANTACHAIRE
PCF 5
7840 9 01 309